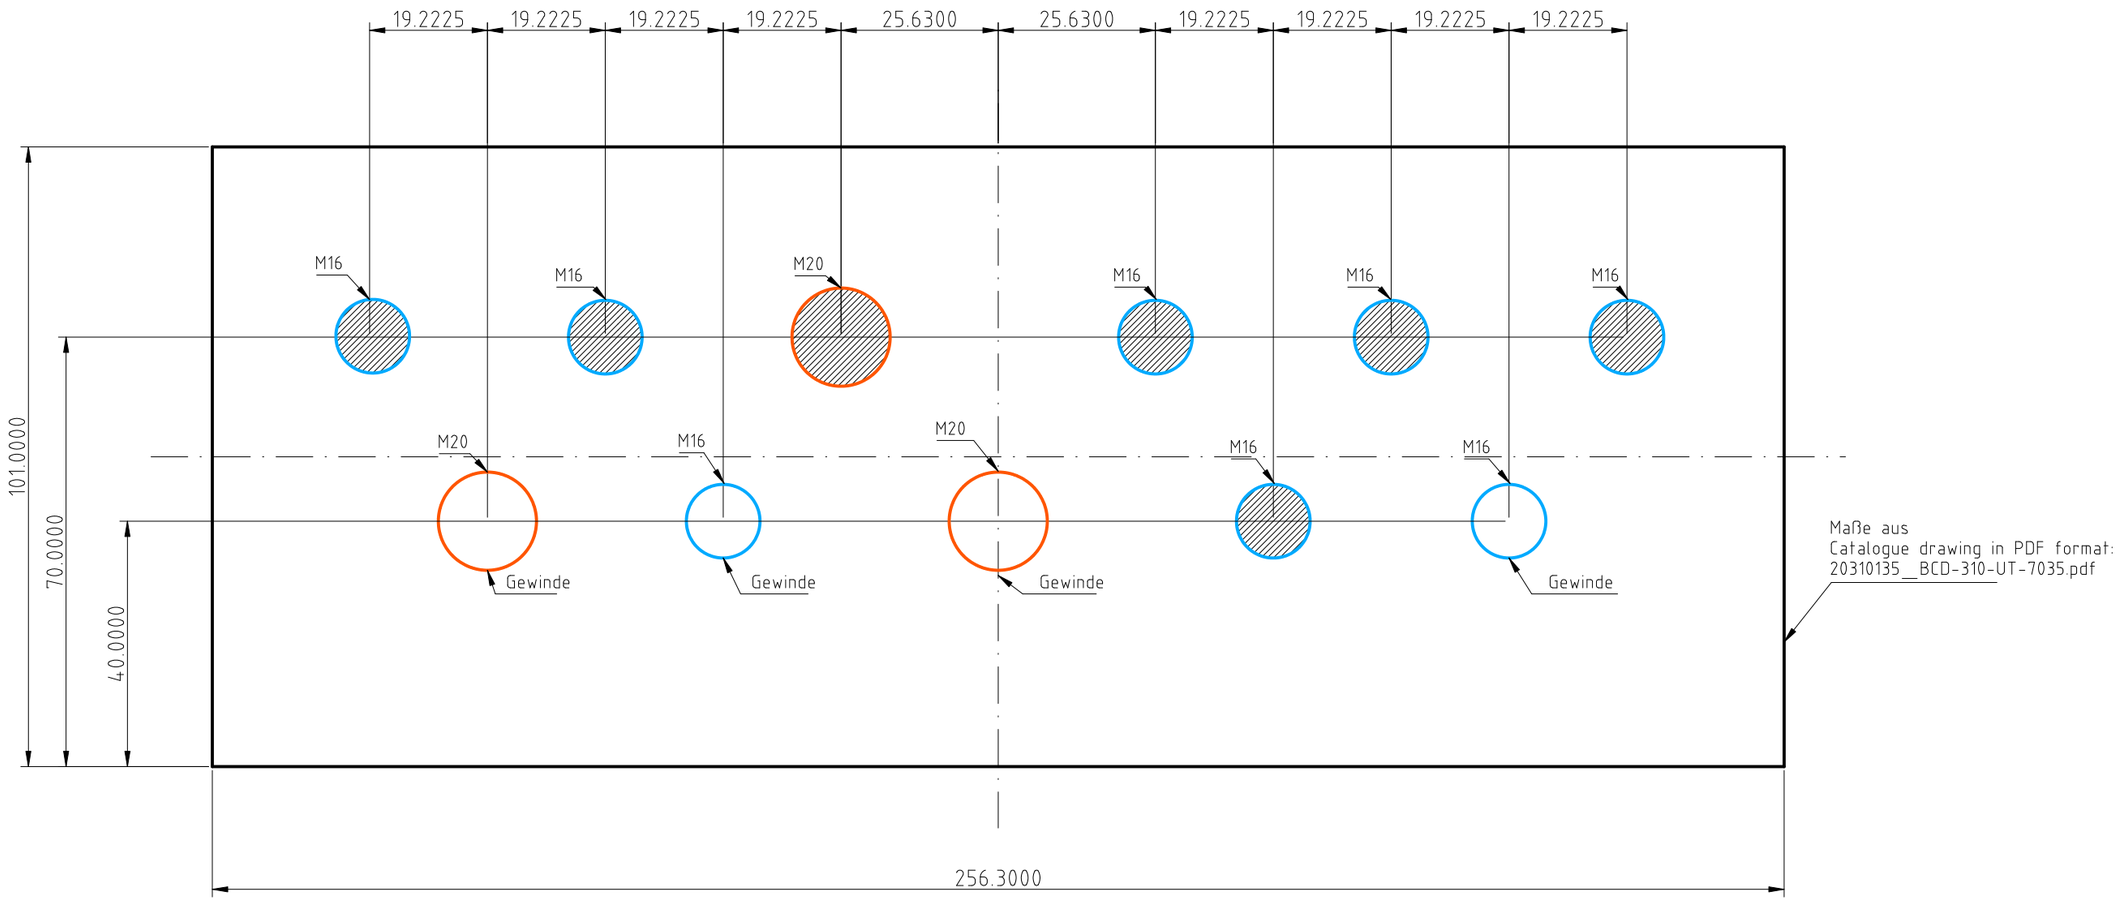

Die Angaben M16 und M20 bezeichnen Ausschnitte bzw. Fräsungen für Kabelverschraubungen.

Die schraffierten Markierungen (alle oberen, eine in der unteren Reihe) sollen nur vorgefräßt werden.

Die Markierungen ohne Schraffur sollen mit Gewinde versehen werden.

All Dimensions in mm

Drawing No Deckel__Bopla__BDC__310__Loescher__Boden.dxf	
Part Name Bopla BDC310 Löcherausschnitte im Boden	Version 0.1.0
Author Stefan Müller	Date 2016-04-07